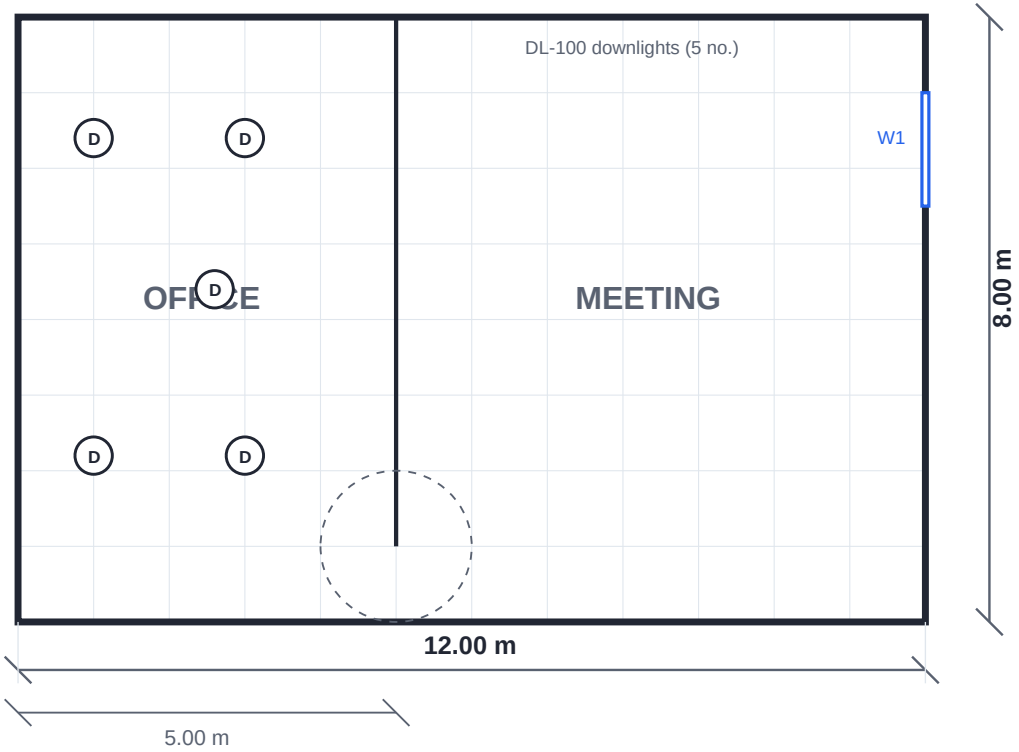

SAMPLE FLOOR PLAN — REV B

SCALE 1:100 @ A4 · DIMENSIONS IN METRES

pdf2takeoff.com — open-source PDF takeoff

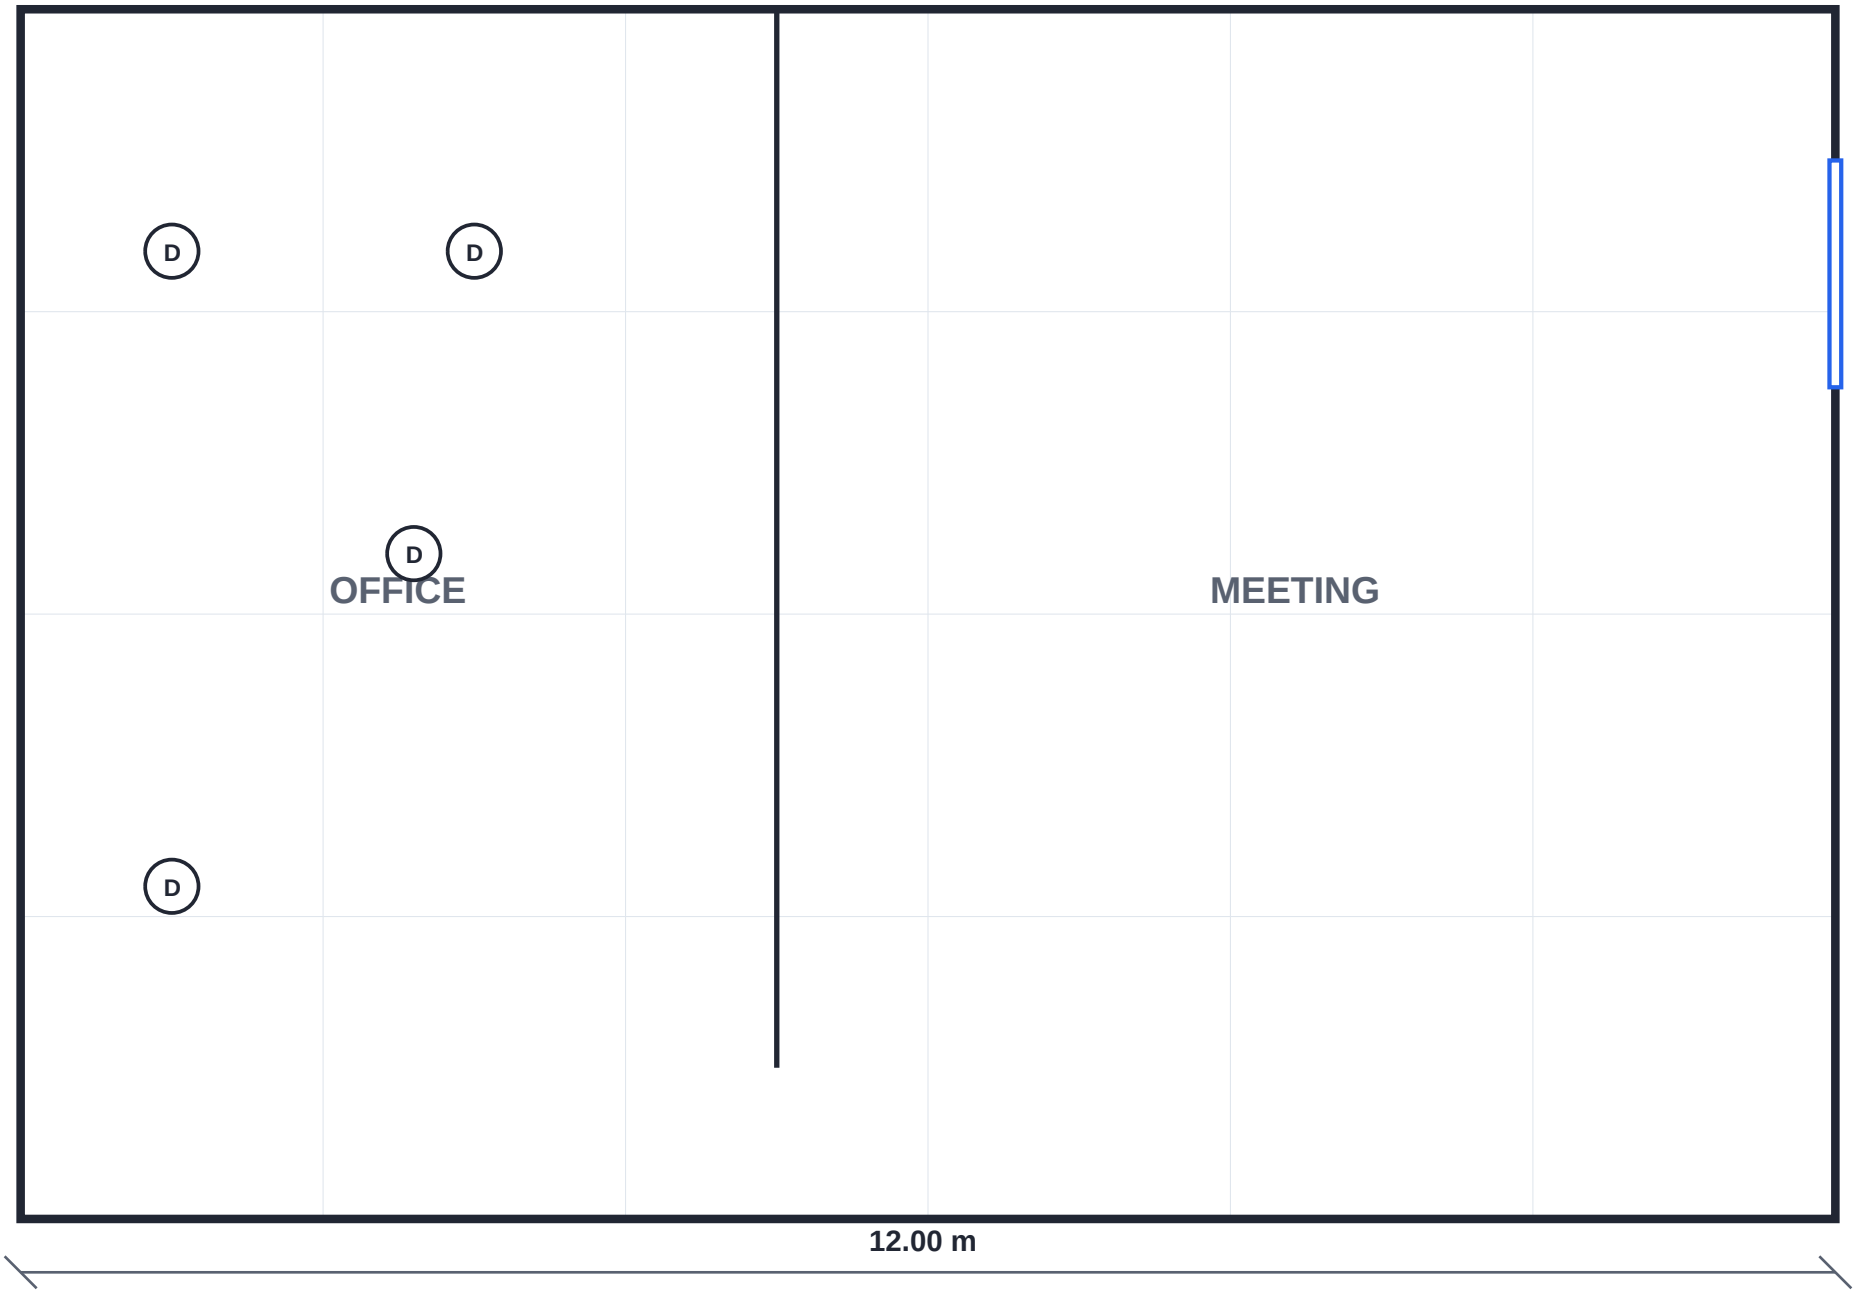

SAMPLE FLOOR PLAN — REV B

SHEET 2 OF 2 · SCALE 1:50 · DIMENSIONS IN METRES